

Опросный лист для заказа УВРУ на два трансформатора с двумя отходящими линиями мощностью более 400 кВА

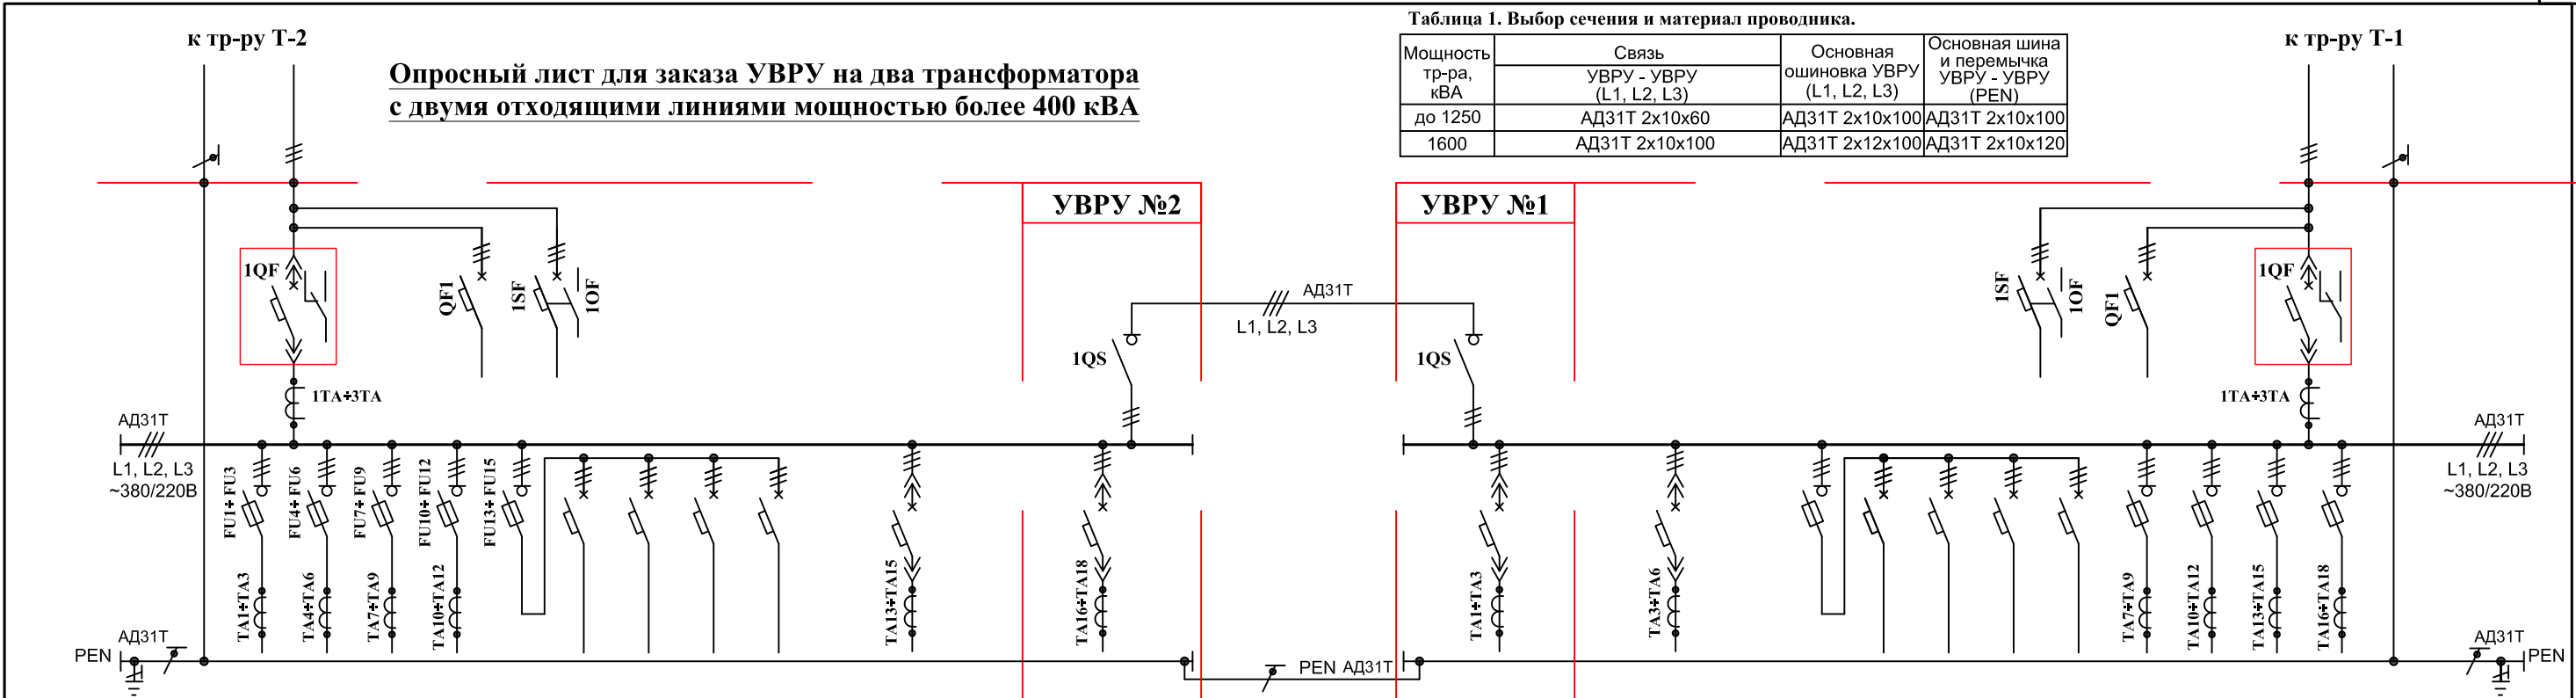
[illegible]

Таблица 2. Выбор оборудования.

Поз. обозначение	Тип оборудования		Количество		Примечание
			УВРУ №1	УВРУ №2	
1QF	Автоматический выключатель *	BA50-45Протон25(Протон40) с МРТпроGF	1	1	Iном=
		BA50-45 DMX с GF+			
		HGS25B (HGS32B) с GPR-LP (Hyundai)			
		HGN25B (HGN32B) с GPR-LP (Hyundai)			
		Masterpact NW25 (NW32) с Micrologic 6.0A			
		OptiMat A с MR 8.0 (КЭАЗ)			
		NA8G с расцепителем M (Chint)			
TA1+TA3	Трансформатор тока на вводе*	ТШП-0,66 кл.т. 0,5S (1500/5; 2000/5)	3	3	Iном=
		ТШЛ-0,66 кл.т. 0,5S (2500/5; 3000/5)			
		MAK-ru 86/60 кл.т. 0,5S (1500/5)			
		MAK-ru 140/100 кл.т. 0,5S (2000/5; 2500/5; 3000/5)			
1QS	Выключатель нагрузки/рубильник *	OT 2000A (2500A)	1	1	Iном= (с блоком доп. контактов)
		OptiSwitch DI 2000A (2500A)			
		I.SE.RE 1800A (2400A)			
QS1+QS5	Планочные предохранители-выключатели-разъединители *	APATOR ARS-3-1S-TM2	5	5	Iном=630 А
		Jean Muller SL3-3			
		OptiVert 3-1-M			
FU1+FU15	Плавкие предохранители серии ППН-39 *				габарит 3 (630А)
TA1+TA18	Трансформатор тока на отходящих линиях*				см. таблицу 3
QF1	Автоматический выключатель BA47-125 3С 15кА		1	1	Iном=100 А
QF2	Автоматический выключатель модульный BA47-29-3С		1	1	Iном=16 А
QF3	Автоматический выключатель модульный BA47-29-3С		1	1	Iном=32 А
QF4	Автоматический выключатель модульный BA47-29-3С		1	1	Iном=40 А
QF5	Автоматический выключатель модульный BA47-29-3С		1	1	Iном=63 А
1SF	Автоматический выключатель модульный BA47-100 3С с блок-контактом		1	1	Iном=10 А
QF6, QF7	Автоматический выключатель *	BA50-45Протон25 с МРТПро (In=800;1000;1250; 1600; 2000; 2500 А)	2	2	Iном=
		BA50-45 DMX с GF+ (In=800; 1000; 1250; 1600; 2000; 2500 А)			
		Hyundai HGN/HGS с GPR-LR (In=800; 1000; 1250; 1600; 2000; 2500 А)			


Таблица 1. Выбор сечения и материал проводника.

Мощность тр-ра, кВА	Связь	Основная ошиновка УВРУ (L1, L2, L3)	Основная шина и перемычка УВРУ-УВРУ (PEN)
	УВРУ - УВРУ (L1, L2, L3)		
до 1250	АДЗ1Т 2х10х60	АДЗ1Т 2х10х100	АДЗ1Т 2х10х100
1600	АДЗ1Т 2х10х100	АДЗ1Т 2х12х100	АДЗ1Т 2х10х120

Таблица 3. Выбор ТТ на отходящих линиях.

Тип оборудования	Тип трансформаторов тока
ППВР (QS1+QS5)	ТШП-0,66 кл.т. 0,5S: 100/5; 150/5; 200/5; 250/5; 300/5; 400/5; 500/5; 600/5 А
	МАК-ру 62/30 кл.т. 0,5S: 100/5; 150/5; 200/5; 250/5; 300/5; 00/5; 500/5; 600/5 А
АВ (QF6, QF7)	ТШП-0,66 кл.т. 0,5S: 600/5; 750/5; 800/5; 1000/5; 1200/5; 1500/5; 2000/5 А
	ТШЛ-0,66 кл.т. 0,5S: 2500/5
	МАК-ру 86/60 кл.т. 0,5S: 600/5; 750/5; 800/5; 1000/5; 1200/5; 1250/5; 1500/5 А
	МАК-ру 140/100 кл.т. 0,5S: 1600/5; 2000/5; 2500/5 А

План расположения

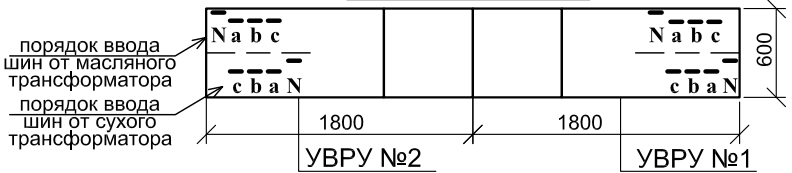

Примечание: УБРУ №2 УБРУ №1

* - количество, номинал, тип указать при привязке проекта

На резервных линиях аппараты защиты, приборы учета и трансформаторы тока не устанавливаются.

Предусматривается место под их установку.

Изм.	Кол.уч	Лист	№ док	Подпись	Дата					
ГИП								Стадия	Лист	Листов
Разработал										
Проверил										
						Опросный лист для заказа УВРУ на два трансформатора с двумя отходящими линиями мощностью более 400 кВА		ООО "ЭМ 55"		
Н.контроль										