

Согласовано

Инв. № подл.	Подпись и дата	Взам. инв. №	

Опросный лист для заказа УВРУ на один трансформатор с одной отходящей линией мощностью более 400 кВА

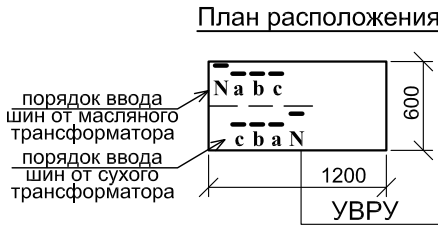
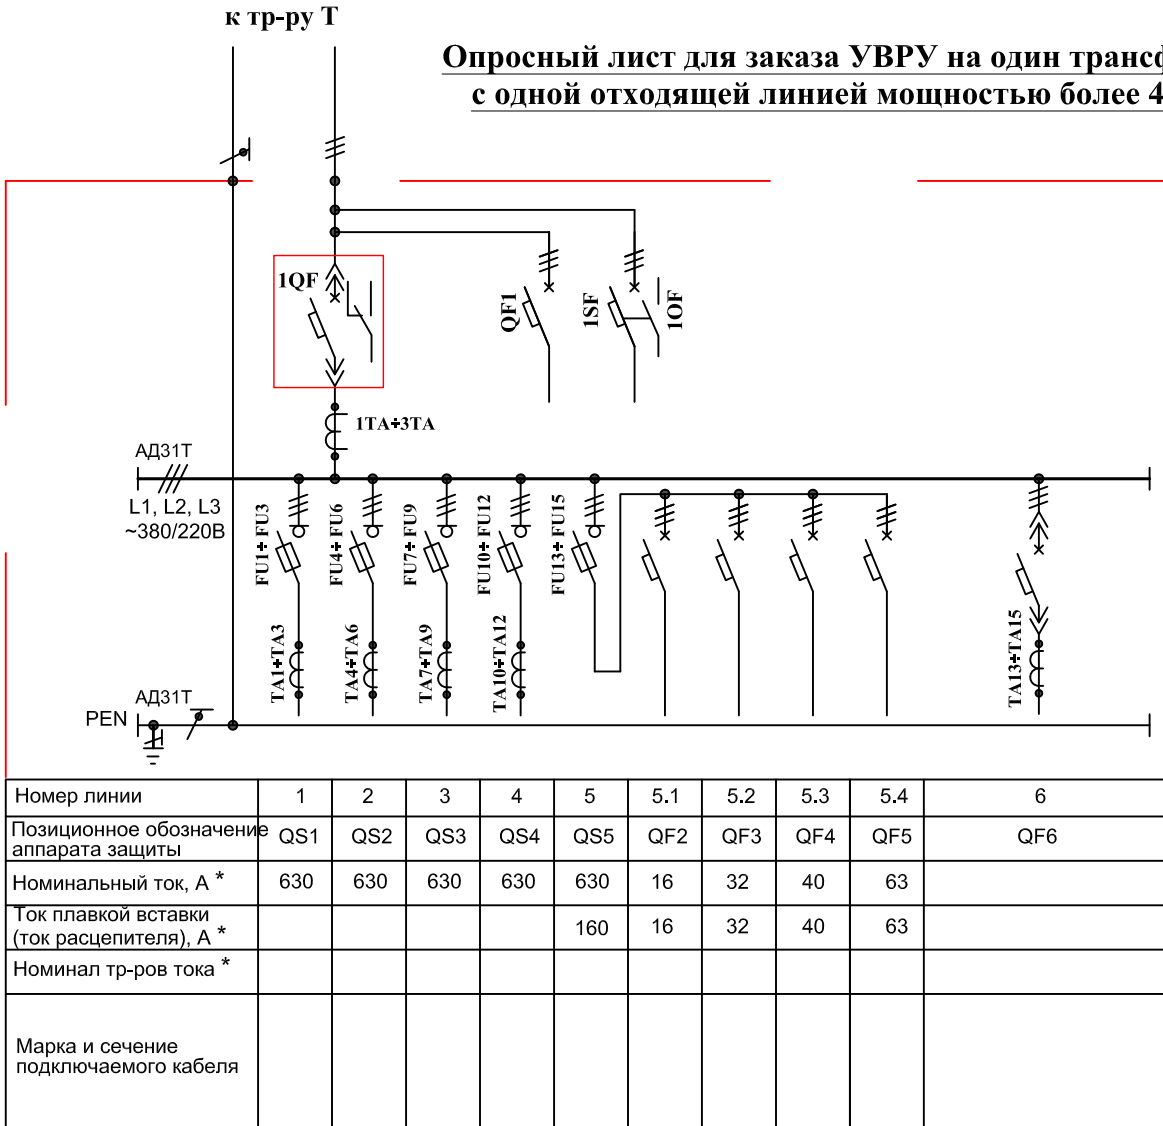


Таблица 1. Выбор сечения и материал проводника.

Мощность тр-ра, кВА	Основная ошиновка УВРУ (L1, L2, L3)	Основная шина (PEN)
до 1250	АД31Т 2х10х100	АД31Т 2х10х100
1600	АД31Т 2х12х100	АД31Т 2х10х120

Таблица 2. Выбор оборудования.

Поз. обозначение	Тип оборудования		Кол-во	Примечание
1QF	Автоматический выключатель *	BA50-45Про Протон25(Протон40) с МРТпроGF	1	I _{ном} =
		BA50-45 DMX с GF+		
		HGS25B (HGS32B) с GPR-LP (Hyundai)		
		HGN25B (HGN32B) с GPR-LP (Hyundai)		
		Masterpact NW25 (NW32) с Micrologic 6.0A		
		OptiMat A с MR 8.0 (КЭАЗ)		
TA1+TA3	Трансформатор тока на вводе*	NA8G с расцепителем М (Chint)	3	I _{ном} =
		ТШП-0,66 кл.т. 0,5S (1500/5; 2000/5)		
		ТШЛ-0,66 кл.т. 0,5S (2500/5; 3000/5)		
		МАК-ру 86/60 кл.т. 0,5S (1500/5)		
QS1+QS5	Планочные предохранители-выключатели-разъединители *	МАК-ру 140/100 кл.т. 0,5S (2000/5; 2500/5; 3000/5)	5	I _{ном} =630 А
		APATOR ARS-3-1S-TM2		
		Jean Muller SL3-3		
FU1+FU15	Плавкие предохранители серии ППН-39 *	OptiVert 3-1-M		габарит 3 (630A)
TA1+TA15	Трансформатор тока на отходящих линиях*			см. таблицу 3
QF1	Автоматический выключатель BA47-125 3С 15кА		1	I _{ном} =100 А
QF2	Автоматический выключатель модульный BA47-29-3С		1	I _{ном} =16 А
QF3	Автоматический выключатель модульный BA47-29-3С		1	I _{ном} =32 А
QF4	Автоматический выключатель модульный BA47-29-3С		1	I _{ном} =40 А
QF5	Автоматический выключатель модульный BA47-29-3С		1	I _{ном} =63 А
1SF	Автоматический выключатель модульный BA47-100 3С с блок-контактом		1	I _{ном} =10 А
QF6	Автоматический выключатель *	BA50-45Про Протон25 с МРТПро (I _н =800;1000;1250; 1600; 2000; 2500 А)	1	I _{ном} =
		BA50-45 DMX с GF+ (I _н =800; 1000; 1250; 1600; 2000; 2500 А)		
		Hyundai HGN/HGS с GPR-LR (I _н =800; 1000; 1250; 1600; 2000; 2500 А)		

Таблица 3. Выбор ТТ на отходящих линиях.

Тип оборудования	Тип трансформаторов тока
ППВР (QS1+QS5)	ТШП-0,66 кл.т. 0,5S: 100/5; 150/5; 200/5; 250/5; 300/5; 400/5; 500/5; 600/5 А
	МАК-ру 62/30 кл.т. 0,5S: 100/5; 150/5; 200/5; 250/5; 300/5; 00/5; 500/5; 600/5 А

Примечание:

* - количество, номинал, тип указать при привязке проекта

На резервных линиях аппараты защиты, приборы учета и трансформаторы тока не устанавливаются. Предусматривается место под их установку.

Изм.	Кол.уч	Лист	№ док	Подпись	Дата				
ГИП							Стадия	Лист	Листов
Разработал									
Проверил									
						Опросный лист для заказа УВРУ на один трансформатор с одной отходящей линией мощностью более 400 кВА	ООО "ЭМ 55"		
Н.контроль									