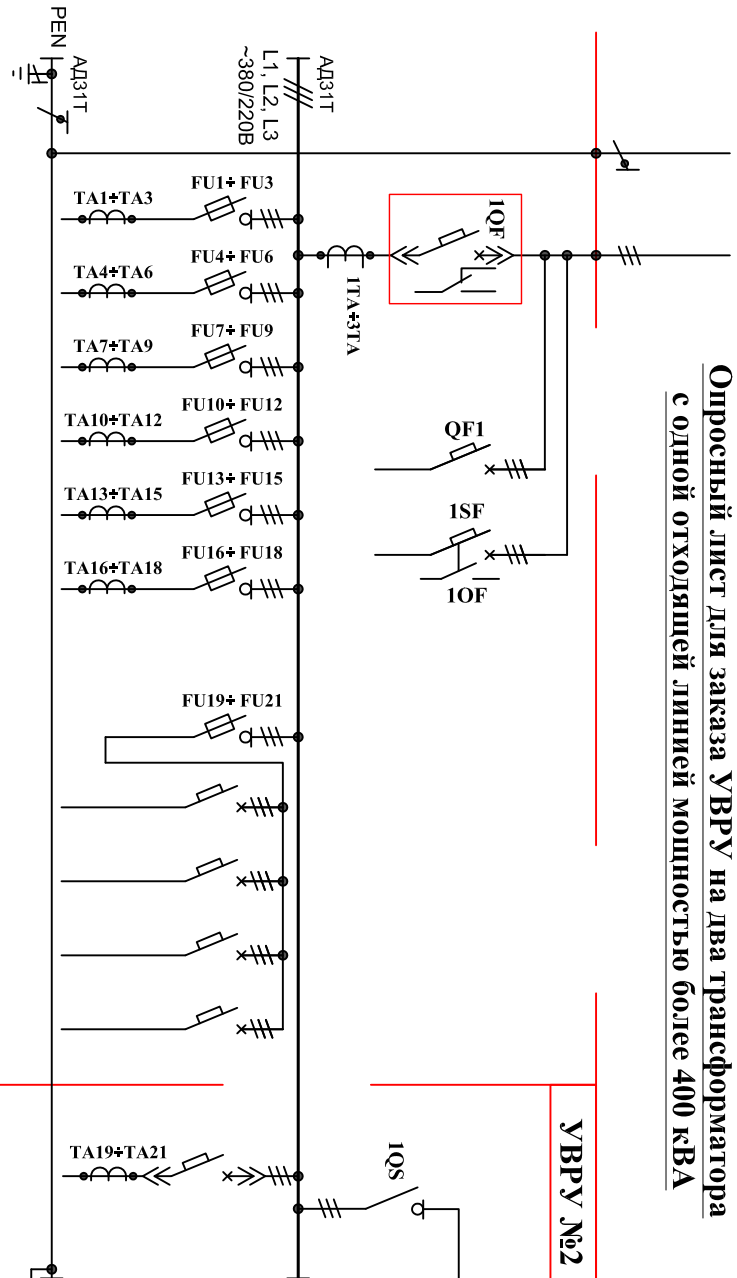


κ TP-py T-2

Опресный лист для заказа УВРУ на два трансформатора с одной отходящей линией мощностью более 400 кВА

[illegible]

Марка и сечение
подключаемого кабеля

Таблица 2. Выбор оборудования.

Поз. обозначение	Тип оборудования	Количество		Примечание
		УВРУ №1	УВРУ №2	
1QF Автоматический выключатель *	BA50-45Прото25(Прото40) с MRТпроGF			Inном=
	BA50-45 DMX с GF+			
	HGS25B (HGS32B) с GPR-LP (Hupidal)	1	1	
	HGN25B (HGN32B) с GPR-LP (Hupidal)			
	Masterpract NW25 (NW32) с Micrologic 6.0A			
	Optimat A с MR 8.0 (KЭA3)			
NA8G с расцепителем M (Chint)				
ТШПТ-0,66 кл.т. 0,5S (1500/5; 2000/5)				
ТШПТ-0,66 кл.т. 0,5S (2500/5; 2000/5)				

Инв. № подл.	Подпись и дата	Взам. инв. №				
	TA1+TA3	трансформатор тока на вводе *	3	3	Inom=	
	1QS	Выключатель наружки/рубильник *	МАК-пу 86/60 кп.т. 0,5S (1500/5)			Inom= (с блоком доп. контактов)
			МАК-пу 140/100 кп.т. 0,5S (2000/5; 2500/5; 3000/5)			
			OT 2000A (2500A)			
			OptiSwitch DI 2000A (2500A)			
	QS1+QS7	Плановые предохранители-выключатели-разъединители *	ISE.RE 1800A (2400A)	1	1	Inom=630 A
			APATOR ARS-3-IS-TM2			
			Jean Muller SL3-3			
	FU1+FU21	Плавкие предохранители серии ППН-39 *				габарит 3 (630/см. таблицу 3
	TA1+TA21	Трансформатор тока на отходящих линиях*				
QF1	Автоматический выключатель ВА47-125 3С 15kA	1	1	1	Inom=100 A	
QF2	Автоматический выключатель модульный ВА47-29-3С	1	1	1	Inom=16 A	
QF3	Автоматический выключатель модульный ВА47-29-3С	1	1	1	Inom=32 A	
QF4	Автоматический выключатель модульный ВА47-29-3С	1	1	1	Inom=40 A	
QF5	Автоматический выключатель модульный ВА47-29-3С	1	1	1	Inom=63 A	
1SF	Автоматический выключатель модульный ВА47-100 3С с блок-контактом	1	1	1	Inom=10 A	
QF6	Автоматический выключатель *	ВАЗО-45Протон25 с МРППро (In=800;1000;1250;1600;2000;2500 A)			Inom=	
		BA50-45 DMX с GF+ (In=800; 1000; 1250; 1600; 2000; 2500 A)				
		Huponda HGN/HGS с GPR-LR (In=800; 1000; 1250; 1600; 2000; 2500 A)				

Таблица 1. Выбор сечения и материал проводника.

Мощность тр-ра, кВА	Связь УВРУ - УВРУ (L1, L2, L3)	Основная ошинная УВРУ (L1, L2, L3)	Основная шина и перемычка УВРУ - УВРУ (PEN)
до 1250	АДЗ1Т 2х10х60	АДЗ1Т 2х10х100	АДЗ1Т 2х10х100
1600	АДЗ1Т 2х10х100	АДЗ1Т 2х12х100	АДЗ1Т 2х10х120

к тp-пy T-1


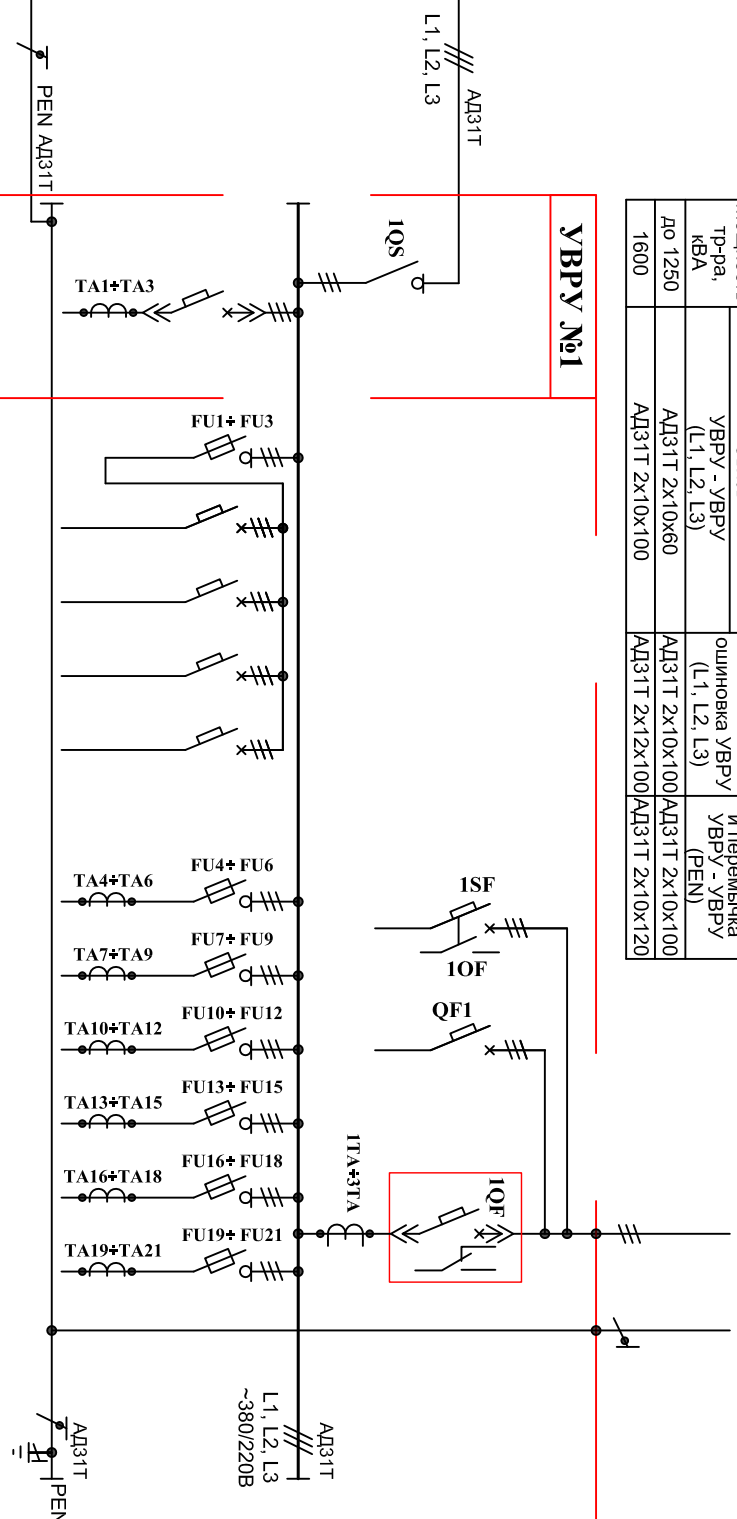
[illegible]

Таблица 3. Выбор ТТ на отходящих линиях

Тип оборудования	Тип трансформаторов тока
ППВР (QS1+QS7)	ТШП-0,66 кл.т. 0,5S; 100/5; 150/5; 200/5; 250/5; 300/5; 400/5; 500/5; 600/5 А МАК-п 62/30 кл.т. 0,5S; 100/5; 150/5; 200/5; 250/5; 300/5; 00/5; 500/5; 600/5 А ТШП-0,66 кл.т. 0,5S; 600/5; 750/5; 800/5; 1000/5; 1200/5; 1500/5; 2000/5 А
AB (Qr6)	ТШП-0,66 кл.т. 0,5S; 2500/5 МАК-п 86/60 кл.т. 0,5S; 600/5; 750/5; 800/5; 1000/5; 1200/5; 1250/5; 1500/5 А МАК-п 140/100 кл.т. 0,5S; 1600/5; 2000/5; 2500/5 А

План расположения

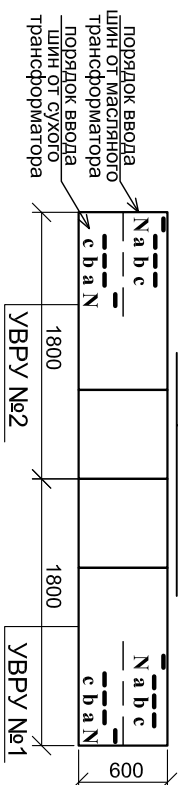

Примечание:

* - количество, номинал, тип указать при привязке проекта

На резервных линиях аппараты защиты, приборы учета и трансформаторы тока не устанавливаются.

Предусматривается место под их установку

Изм.	Кол.уч	Лист	№ док	Подпись	Дата				
ГИП									
Разработал									
Проверил									
Н.контроль						Опросный лист для заказа УВРУ на два трансформатора с одной отходящей линией мощностью более 400 кВА			
						Стадия	Лист	Листов	
									ООО "ЭМ 55"