Опросный лист для заказа УВРУ на два трансформатора с двумя отходящими линиями мощностью более 400 кВА

Таблица 1. Выбор сечения и материал проводника.

Мощность тр-ра, кВА	Связь УВРУ - УВРУ (L1, L2, L3)	Основная ошиновка УВРУ (L1, L2, L3)	Основная шина и перемычка УВРУ - УВРУ (PEN)
до 1250	АД31Т 2х10х60	АД31Т 2х10х100	АД31Т 2х10х100
1600	АД31Т 2х10х100	АД31Т 2х12х100	АД31Т 2х10х120

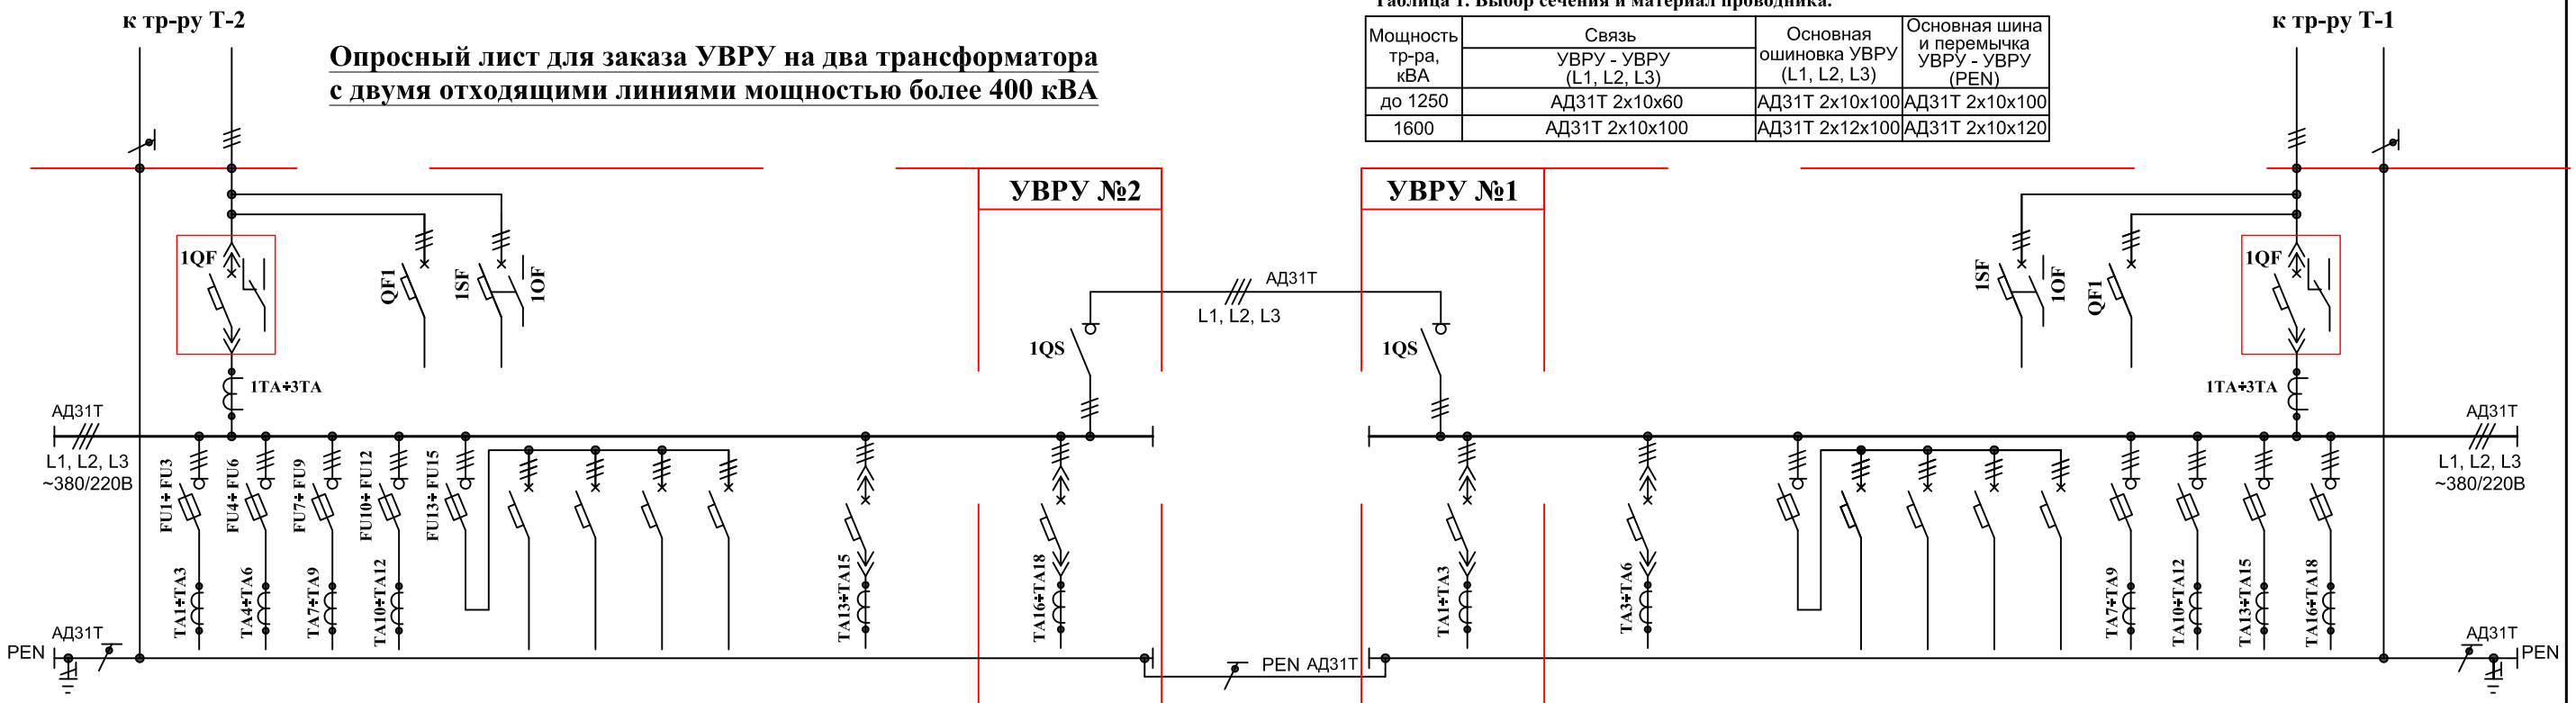

Номер линии	1	2	3	4	5	5.1	5.2	5.3	5.4	6	7		1	2	3	3.1	3.2	3.3	3.4	4	5	6	7	
Позиционное обозначение аппарата защиты	QS1	QS2	QS3	QS4	QS5	QF2	QF3	QF4	QF5	QF6	QF7		QF6	QF7	QS1	QF2	QF3	QF4	QF5	QS2	QS3	QS4	QS5	
Номинальный ток, А *	630	630	630	630	630	16	32	40	63						630	16	32	40	63	630	630	630	630	
Ток плавкой вставки (ток расцепителя), А *					160	16	32	40	63						160	16	32	40	63					
Номинал тр-ров тока *																								
Марка и сечение подключаемого кабеля																								

Таблица 2. Выбор оборудования.

Поз. обозначение	Тип оборудования		Количество УВРУ №1	Количество УВРУ №2	Примечание
1QF	Автоматический выключатель *	ВА50-45Про Протон25(Протон40) с МРТпроGF	1	1	Iном=
		ВА50-45 DMX с GF+			
		HGS25B (HGS32B) с GPR-LP (Hyundai)			
		HGN25B (HGN32B) с GPR-LP (Hyundai)			
		Masterpact NW25 (NW32) с Micrologic 6.0A			
		OptiMat A с MR 8.0 (КЭАЗ)			
		NA8G с расцепителем M (Chint)			
TA1÷TA3	Трансформатор тока на вводе*	ТШП-0,66 кл.т. 0,5S (1500/5; 2000/5)	3	3	Iном=
		ТШЛ-0,66 кл.т. 0,5S (2500/5; 3000/5)			
		МАК-ru 86/60 кл.т. 0,5S (1500/5)			
		МАК-ru 140/100 кл.т. 0,5S (2000/5; 2500/5; 3000/5)			
1QS	Выключатель нагрузки/ рубильник *	ОТ 2000А (2500А)	1	1	Iном= (с блоком доп. контактов)
		OptiSwitch DI 2000A (2500A)			
		I.SE.RE 1800A (2400A)			
QS1÷QS5	Планочные предохранители-выключатели-разъединители *	APATOR ARS-3-1S-TM2	5	5	Iном=630 А
		Jean Muller SL3-3			
		OptiVert 3-1-M			
FU1÷FU15	Плавкие предохранители серии ППН-39 *				габарит 3 (630А)
TA1÷TA18	Трансформатор тока на отходящих линиях*				см. таблицу 3
QF1	Автоматический выключатель ВА47-125 3С 15кА		1	1	Iном=100 А
QF2	Автоматический выключатель модульный ВА47-29-3С		1	1	Iном=16 А
QF3	Автоматический выключатель модульный ВА47-29-3С		1	1	Iном=32 А
QF4	Автоматический выключатель модульный ВА47-29-3С		1	1	Iном=40 А
QF5	Автоматический выключатель модульный ВА47-29-3С		1	1	Iном=63 А
1SF	Автоматический выключатель модульный ВА47-100 3С с блок-контактом		1	1	Iном=10 А
QF6, QF7	Автоматический выключатель *	ВА50-45Про Протон25 с МРТПро (Iн=800;1000;1250; 1600; 2000; 2500 А)	2	2	Iном=
		ВА50-45 DMX с GF+ (Iн=800; 1000; 1250; 1600; 2000; 2500 А)			
		Hyundai HGN/HGS с GPR-LR (Iн=800; 1000; 1250; 1600; 2000; 2500 А)			

Таблица 3. Выбор ТТ на отходящих линиях.

Тип оборудования	Тип трансформаторов тока
ППВР (QS1÷QS5)	ТШП-0,66 кл.т. 0,5S: 100/5; 150/5; 200/5; 250/5; 300/5; 400/5; 500/5; 600/5 А
	МАК-ru 62/30 кл.т. 0,5S: 100/5; 150/5; 200/5; 250/5; 300/5; 00/5; 500/5; 600/5 А
АВ (QF6, QF7)	ТШП-0,66 кл.т. 0,5S: 600/5; 750/5; 800/5; 1000/5; 1200/5; 1500/5; 2000/5 А
	ТШЛ-0,66 кл.т. 0,5S: 2500/5
	МАК-ru 86/60 кл.т. 0,5S: 600/5; 750/5; 800/5; 1000/5; 1200/5; 1250/5; 1500/5 А
	МАК-ru 140/100 кл.т. 0,5S: 1600/5; 2000/5; 2500/5 А

План расположения

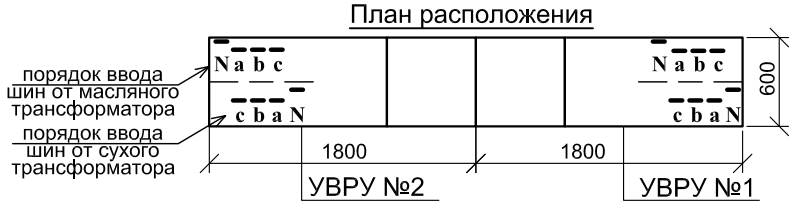

Примечание:
*** - количество, номинал, тип указать при привязке проекта**
На резервных линиях аппараты защиты, приборы учета и трансформаторы тока не устанавливаются.
Предусматривается место под их установку.

Изм.	Кол.уч	Лист	№ док	Подпись	Дата			
ГИП						Опросный лист для заказа УВРУ на два трансформатора с двумя отходящими линиями мощностью более 400 кВА	Стадия	Лист	Листов
Разработал									
Проверил							ООО "ЭМ 55"		
Н.контроль									

Согласовано | Взам. инв. № | Подпись и дата | Инв. № подл.

Формат А3