

κ TP-py T-2

**Опросный лист для заказа УВРУ на два трансформатора
с отходящими линиями мощностью до 400 кВА**

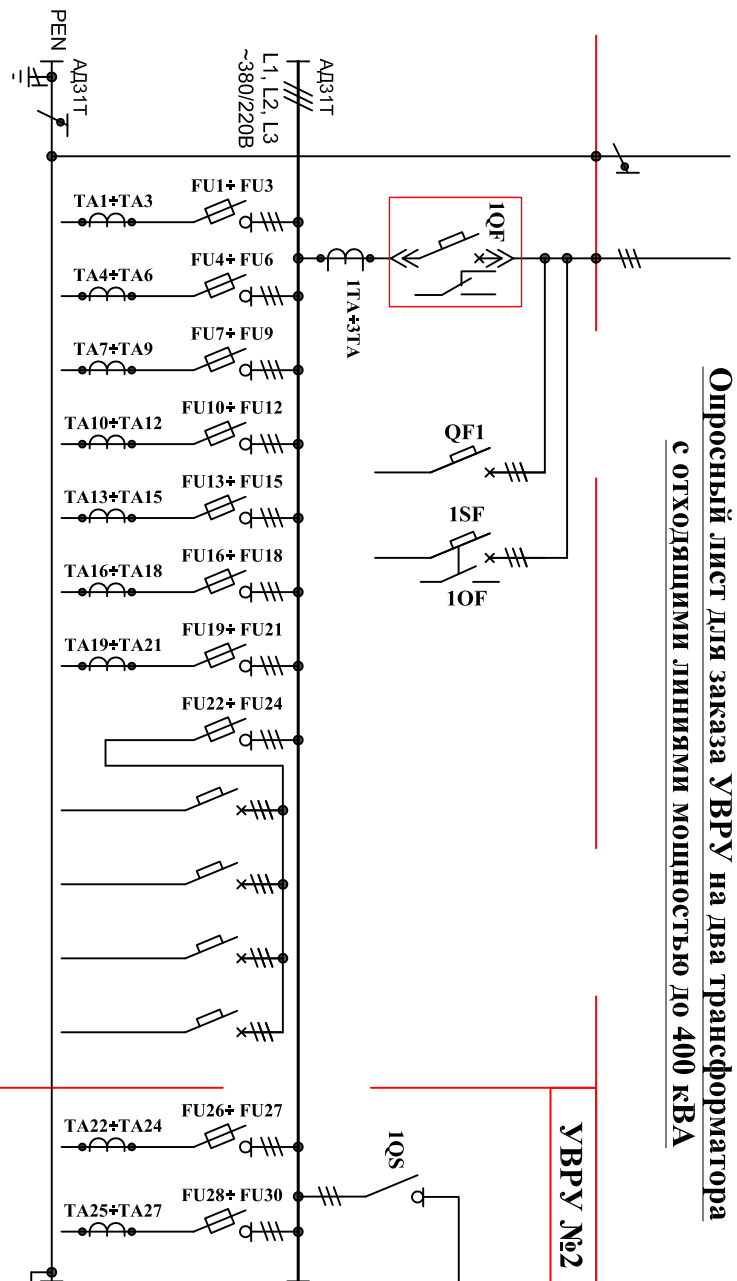


Таблица 1. Выбор сечения и материал проводника.

Мощность тр-ра, кВА	Связь		Основная ошиновка ЛЭУ (Л1, Л2, Л3)	Основная шина и перемычка УВРУ - УВРУ (PEN)
	УВРУ - УВРУ (Л1, Л2, Л3)			
до 1250	АДЗ1Т 2х10х60		АДЗ1Т 2х10х100	АДЗ1Т 2х10х100
1600	АДЗ1Т 2х10х100		АДЗ1Т 2х12х100	АДЗ1Т 2х10х120

к тp-пy T-1

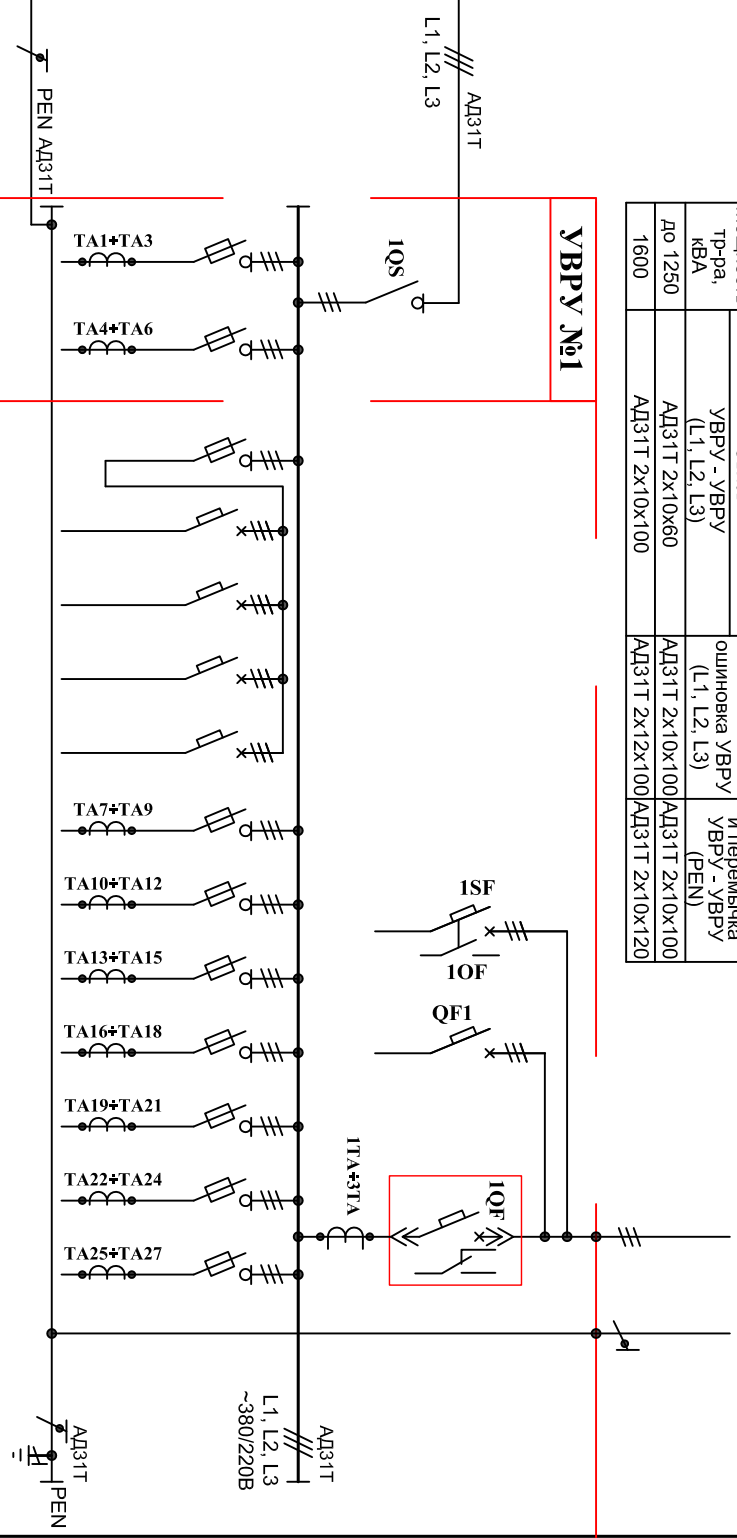
[illegible]


Таблица 2. Выбор оборудования.

Поз. обозначение	Тип оборудования	Количество		Примечание
		УВРУ №1	УВРУ №2	
1QF	Автоматический выключатель *	1	1	Inom=
TA1+TA3	Трансформатор тока на вводе *	3	3	Inom=
1QS	Выключатель нагрузки/ рубильник *	1	1	Inom= (с блоком доп. контактов)
QS1+QS10	Планочные предохранители-выключатели-разъединители *	10	10	Inom=630 A
FU1+FU30	Плавкие предохранители серии ППН-39 *			габарит 3 (630A)
TA1+TA27	Трансформатор тока на отходящих линиях*			см. таблицу 3
QF1	Автоматический выключатель ВА47-125 3С 16кА	1	1	Inom=100 A
QF2	Автоматический выключатель модульный ВА47-29-3С	1	1	Inom=16 A
QF3	Автоматический выключатель модульный ВА47-29-3С	1	1	Inom=32 A
QF4	Автоматический выключатель модульный ВА47-29-3С	1	1	Inom=40 A
QF5	Автоматический выключатель модульный ВА47-29-3С	1	1	Inom=63 A
1SF	Автоматический выключатель модульный ВА47-100 3С с блок-контактом	1	1	Inom=10 A

Таблица 3. Выбор ТТ на отходящих линиях.

Тип оборудования	Тип трансформаторов тока
ЛПБР (QS1+QS10)	ТШП-0,66 кл.т. 0,5S: 100/5; 150/5; 200/5; 250/5; 300/5; 400/5; 500/5; 600/5 А МАК-ш 62/30 кл.т. 0,5S: 100/5; 150/5; 200/5; 250/5; 300/5; 00/5; 500/5; 600/5 А

План расположения

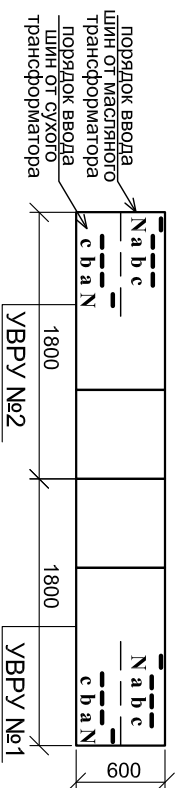

Примечание:

* - количество, номинал, тип указать при привязке проекта
На резервных линиях аппараты защиты, приборы учета и трансформаторы тока не устанавливаются.
Предусматривается место под их установку.

Изм.	Коп.уч	Лист	№ док	Подпись	Дата					
ГП										
Разработал										
Проверил										
Н.контроль										
Опросный лист для заказа УВРУ на два трансформатора с отходящими линиями мощностью до 400 кВА						Стадия	Лист	Листов		
						ООО "ЭМ 55"				